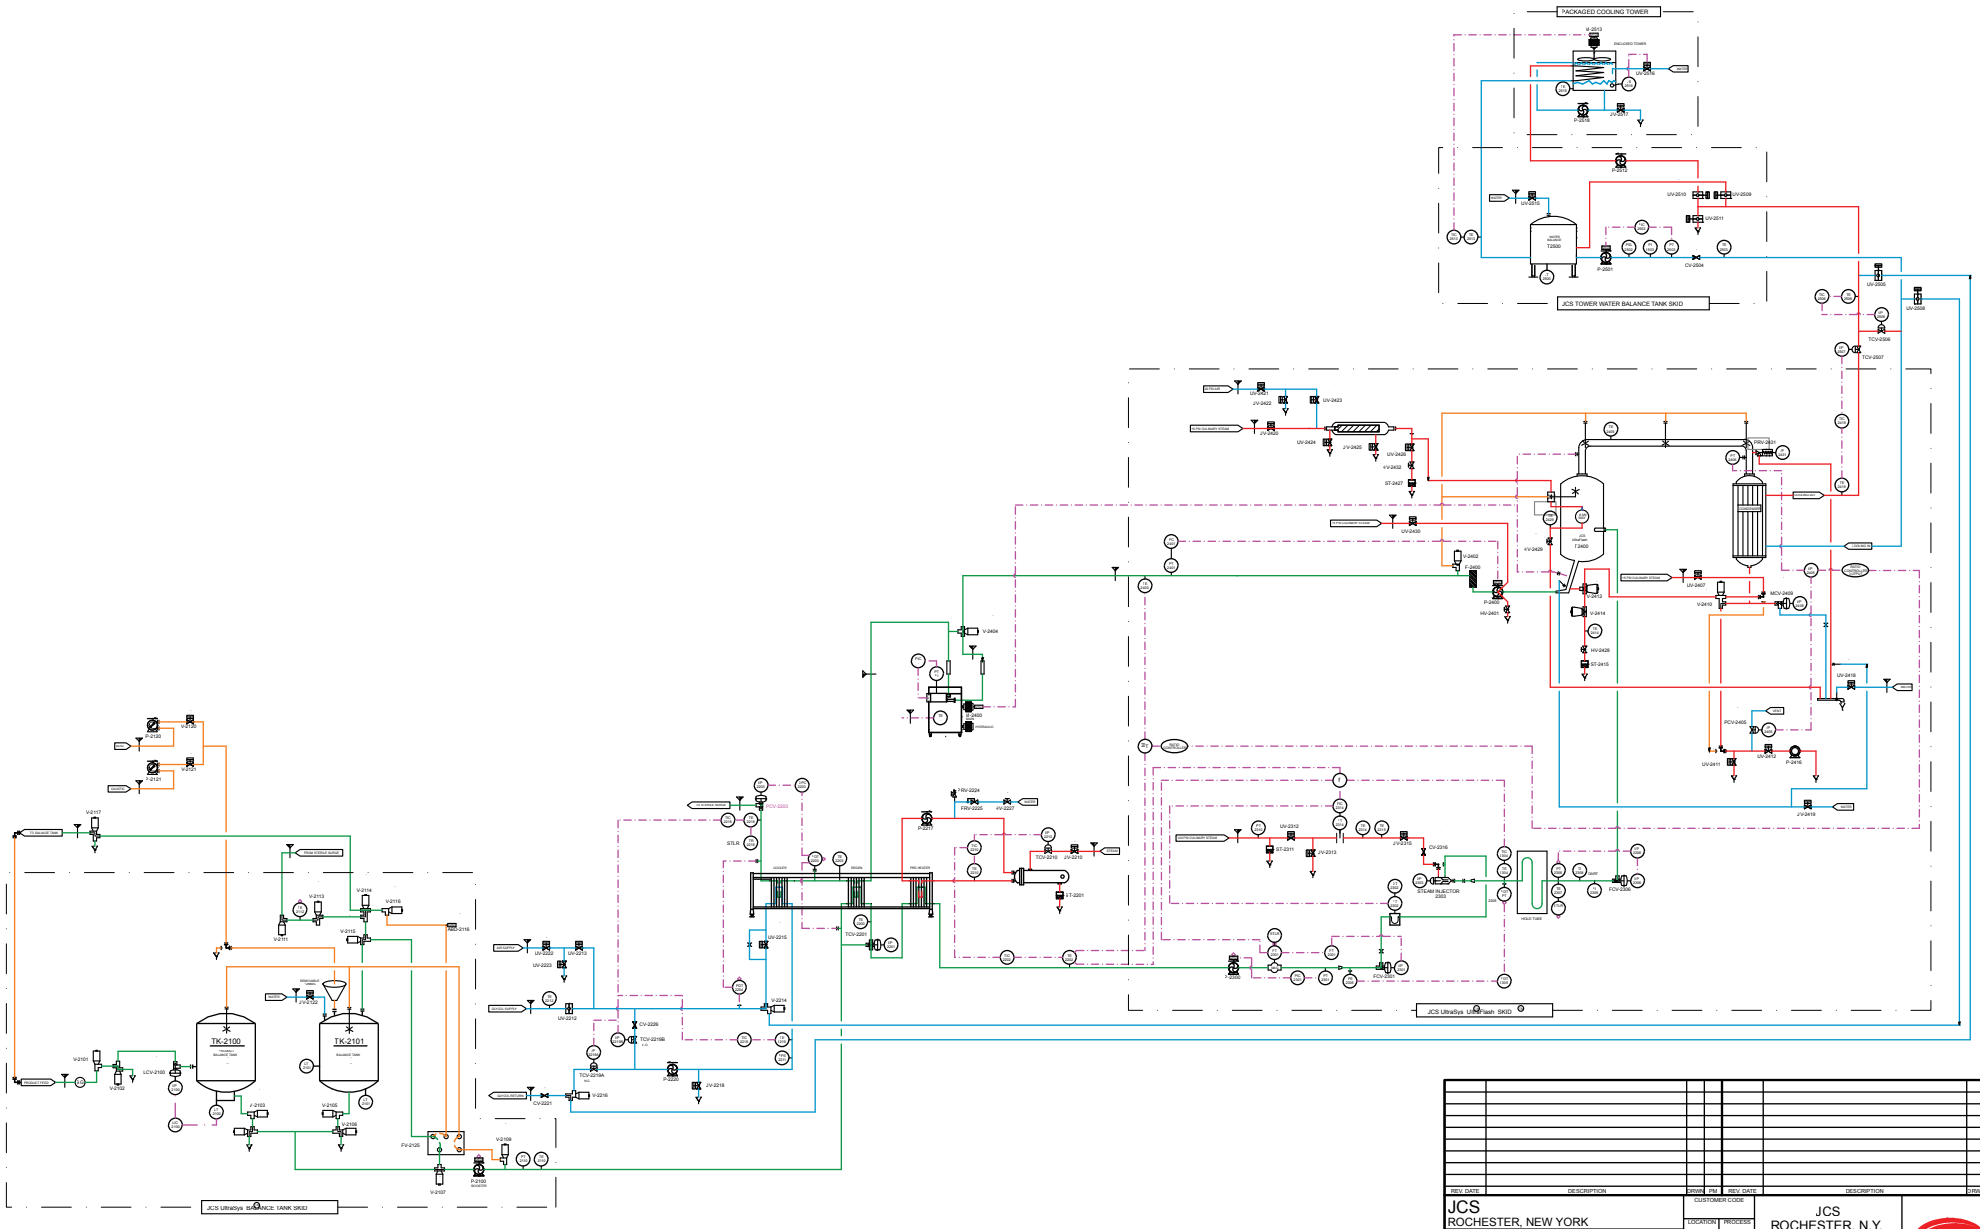

THIS DOCUMENT AND ITS CONTENTS ARE THE EXCLUSIVE PROPERTY OF JCS CONTROLS INC. AND MUST NOT BE REPRODUCED, TRANSMITTED, OR COMMUNICATED WITHOUT PRIOR WRITTEN APPROVAL OF JCS CONTROLS INC. THESE PLANS ARE NOT MADE FOR CONSTRUCTION OR INSTALLATION UNLESS USE FOR THIS PURPOSE HAS BEEN EXPRESSLY APPROVED BY JCS CONTROLS INC. ON THIS DOCUMENT.

DWG NAME: 4156-010A (092309).dwg
JOB# 4156 DIR
MOD. TIME: 9/28/2009 01:55 PM

REV. DATE	DESCRIPTION	DRAWN	REV. DATE	DESCRIPTION	DRAWN

JCS
ROCHESTER, NEW YORK

P&ID
STANDARD ULTRASYS

PROCESS

DRAWN BY	PROJ. MANAGER
CCK	PRF

CUSTOMER CODE

LOCATION	PROCESS
NY	

SCALE

DATE: 8/11/14

JCS
ROCHESTER, N.Y.

PROJECT NO.

DRAWING NO.

JCS Process & Control Systems Engineering